


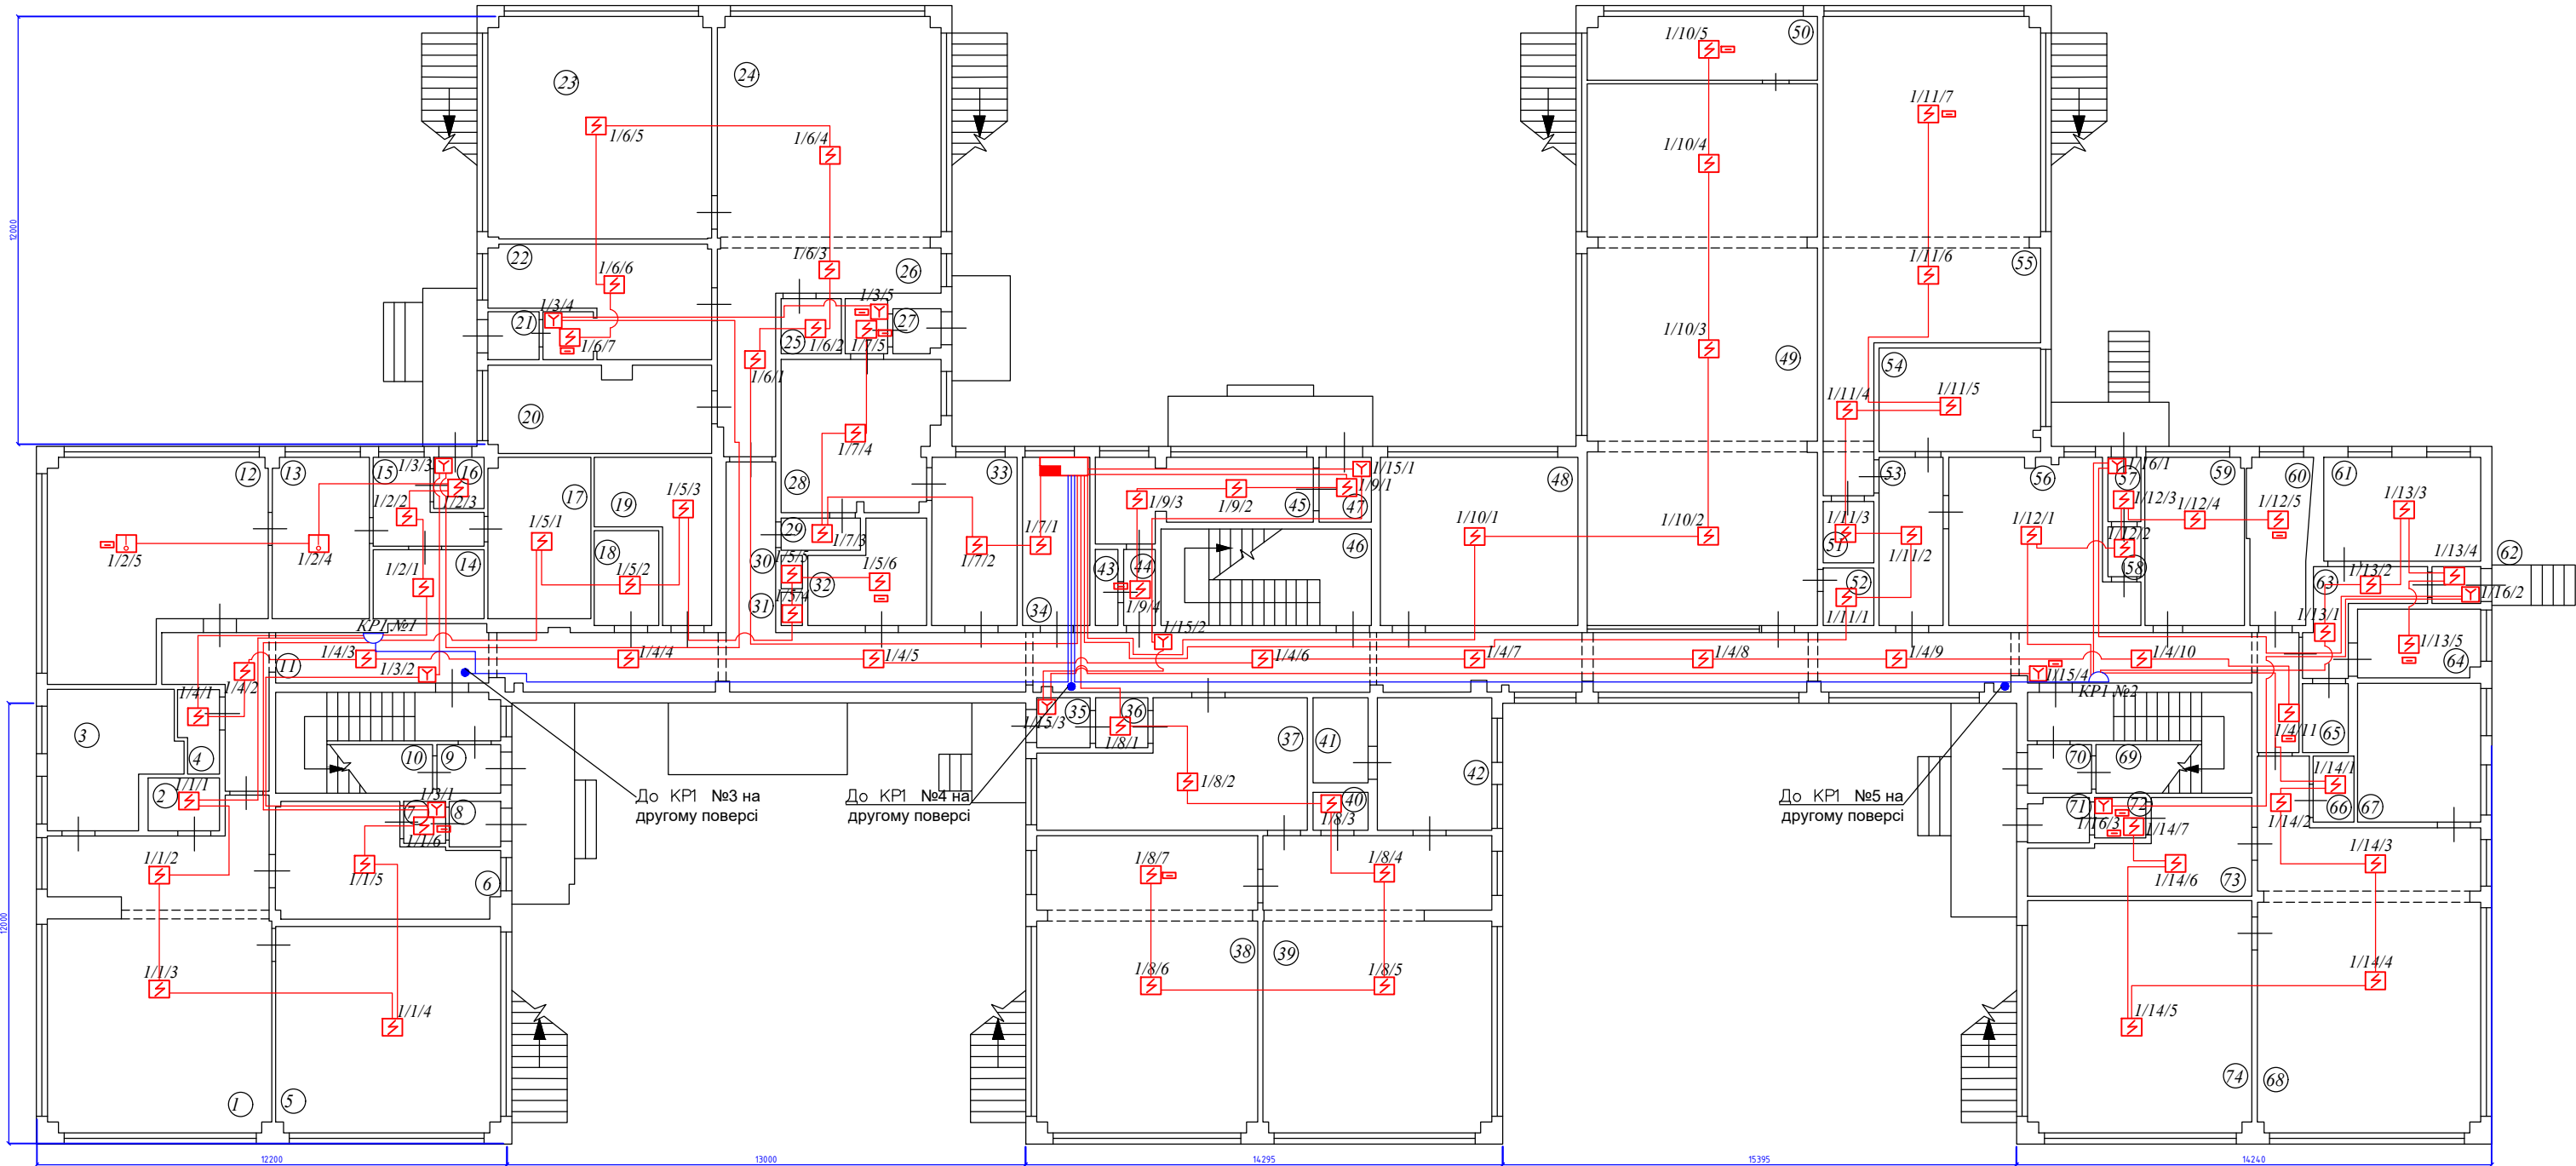


Умовні позначення

	ППКП
	Димовий сповіщувач СПД-3
	Ручний пожежний сповіщувач SPR-1
	Димовий сповіщувач СПД-3
	Коробка розгалужувальна КРП
	Коробка з кінцевим резистором
	Провід ПСВВнг 4х0,4

Експлікація приміщень			Експлікація приміщень			Експлікація приміщень		
№	Назва приміщення	Площа, кв. м	№	Назва приміщення	Площа, кв. м	№	Назва приміщення	Площа, кв. м
1	Ігрова кімната	48,6	26	Тамбур	1,7	53	Коридор	7,8
2	Мийка	2,3	27	Тамбур	1,6	54	Кабінет	12
3	Санвузол	11,7	28	Пральня	17,2	55	Спортивний зал	58,5
4	Роздягальня	2,3	29	Коридор	1,9	56	Кабінет	20,1
5	Кімната відпочинку	35,9	30	Електрощитова	0,6	57	Тамбур	1,6
6	Роздягальня	15,2	31	Електрощитова	0,6	58	Тамбур	1,2
7	Тамбур	1,3	32	Кабінет	8	59	Кабінет	12,6
8	Тамбур	1,7	33	Кабінет	10,7	60	Кабінет	7,3
9	Тамбур	2,3	34	Кабінет	8,5	61	Медпункт	17,1
10	Сходи	13,9	35	Тамбур	1,9	62	Тамбур	1,3
11	Коридор	101,9	36	Тамбур	2	63	Коридор	5,1
12	Кухня	32,5	37	Роздягальня	22	64	Кабінет	6,1
13	Обочевий цех	12,2	38	Кімната відпочинку	48,8	65	Санвузол	1,9
14	Підсобне	4,6	39	Ігрова кімната	45,3	66	Мийка	2,4
15	Коридор	5	40	Мийка	1,6	67	Санвузол	12,1
16	Тамбур	1,9	41	Санвузол	3,8	68	Ігрова кімната	52
17	Комора	11,4	42	Умивальник	11,3	69	Сходи	13,9
18	Побутове приміщення	4,2	43	Санвузол	1,3	70	Тамбур	2,3
19	Склад	9,6	44	Коридор	1,8	71	Тамбур	2
20	Санвузол	16	45	Кабінет	11,1	72	Тамбур	1,5
21	Тамбур	1,8	46	Сходи	11,1	73	Роздягальня	11,8
22	Роздягальня	16,7	47	Тамбур	2,5	74	Кімната відпочинку	38,5
23	Кімната відпочинку	37,5	48	Кабінет	25,3			
24	Ігрова кімната	51,8	49	Музичний зал	92,3			
25	Мийка	3,1	50	Побутова кімната	10,7			
			51	Коридор	2,3			
			52	Побутова кімната	2,1			

						03/2026-СПС-СО		
						Монтаж автоматичної пожежної сигналізації в закладі дошкільної освіти №21 "Горобинка", що розташований за адресою: м. Кропивницький, вул. Марії Примаченко, 4. Коригування		
Змін.	Кільк.	Арк.	№док	Підпис	Дата	Система пожежної сигналізації та система керування евакуюванням в частині оповіщення про пожежу	Стадія	Аркуш
ГП	Черевань				2026		РП	2
Розробив	Патинко				2026			6
Перевірив	Черевань				2026			
Н. Контр.	Черевань				2026	Схема СПС 1-го поверху		
						ТОВ "Пожежно-технічний захист"		

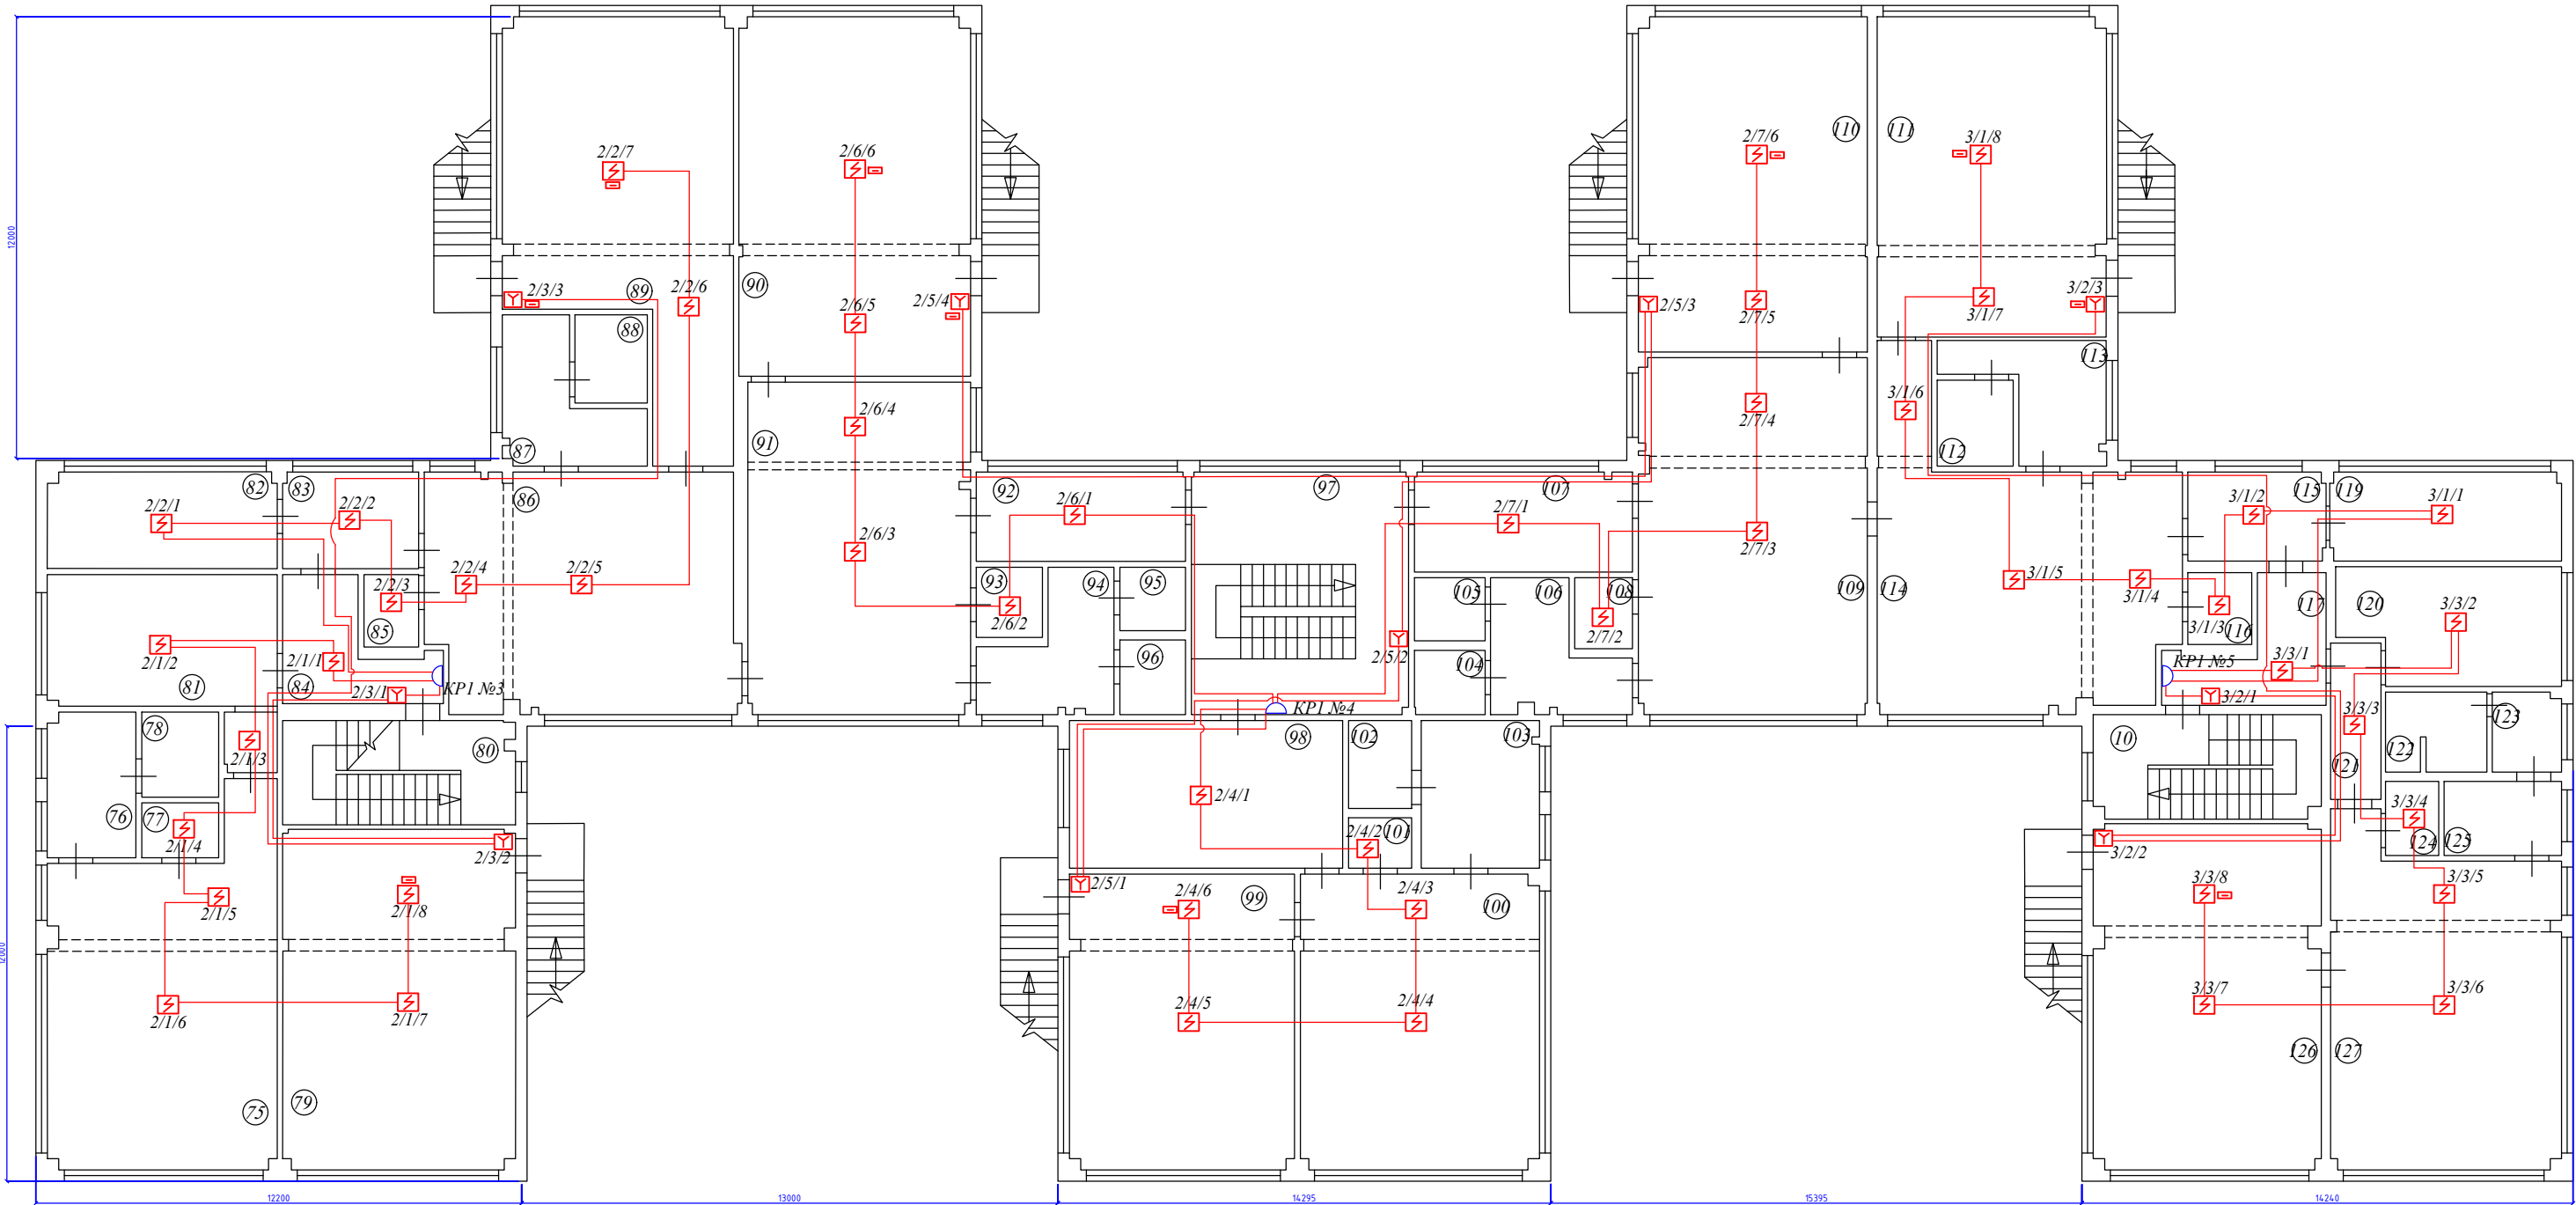


Умовні позначення

	ППКП
	Димовий сповіщувач СПД-3
	Ручний пожежний сповіщувач SPR-1
	Димовий сповіщувач СПД-3
	Коробка розгалужувальна КРІ
	Коробка з кінцевим резистором
	Провід ПСВВнг 4х0,4

Експлікація приміщень			Експлікація приміщень		
№	Назва приміщення	Площа, кв. м	№	Назва приміщення	Площа, кв. м
75	Ігрова кімната	51,3	100	Ігрова кімната	50,1
76	Умивальник	8,9	101	Мийка	2,2
77	Мийка	2,9	102	Санвузол	3,9
78	Санвузол	4,7	103	Умивальник	11,7
79	Кімната відпочинку	54,8	104	Санвузол	2,9
80	Сходи	17,2	105	Санвузол	3,1
81	Роздягальня	23,4	106	Умивальник	9,8
82	Побутове приміщення	14,9	107	Роздягальня	15,1
83	Коридор	9,1	108	Мийка	2,8
84	Коридор	9,5	109	Ігрова кімната	56,2
85	Побутове приміщення	2,7	110	Кімната відпочинку	53,2
86	Ігрова кімната	51,2	111	Кімната відпочинку	50,7
87	Умивальник	10,1	112	Санвузол	4,5
88	Санвузол	4,4	113	Умивальник	9,5
89	Кімната відпочинку	55,4	114	Ігрова кімната	54,4
90	Кімната відпочинку	57,6	115	Коридор	8,5
91	Ігрова кімната	51,4	116	Побутове приміщення	3,2
92	Роздягальня	13	117	Коридор	9,5
93	Мийка	3,2	118	Сходи	16,1
94	Умивальник	8,7	119	Побутове приміщення	14,2
95	Санвузол	2,8	120	Роздягальня	17,1
96	Санвузол	3	121	Коридор	9,5
97	Сходи	25,8	122	Санвузол	5,1
98	Роздягальня	28,1	123	Умивальник	3,7
99	Кімната відпочинку	47,3	124	Мийка	2,7
			125	Умивальник	5,8
			126	Кімната відпочинку	54,2
			127	Ігрова кімната	51,1


						03/2026-СПС-СО		
						Монтаж автоматичної пожежної сигналізації в закладі дошкільної освіти №21 "Горобинка", що розташований за адресою: м. Кропивницький, вул. Марії Примаченко, 4. Коригування		
Змін.	Кільк.	Арк.	№док	Підпис	Дата	Система пожежної сигналізації та система керування евакуюванням в частині оповіщення про пожежу	Стадія	Аркуш
ГП	Черевань				2026		РП	3
Розробив	Патинко				2026			6
Перевірив	Черевань				2026	Схема СПС 2-го поверху		
						ТОВ "Пожежно-технічний захист"		
Н. Контр.	Черевань				2026			

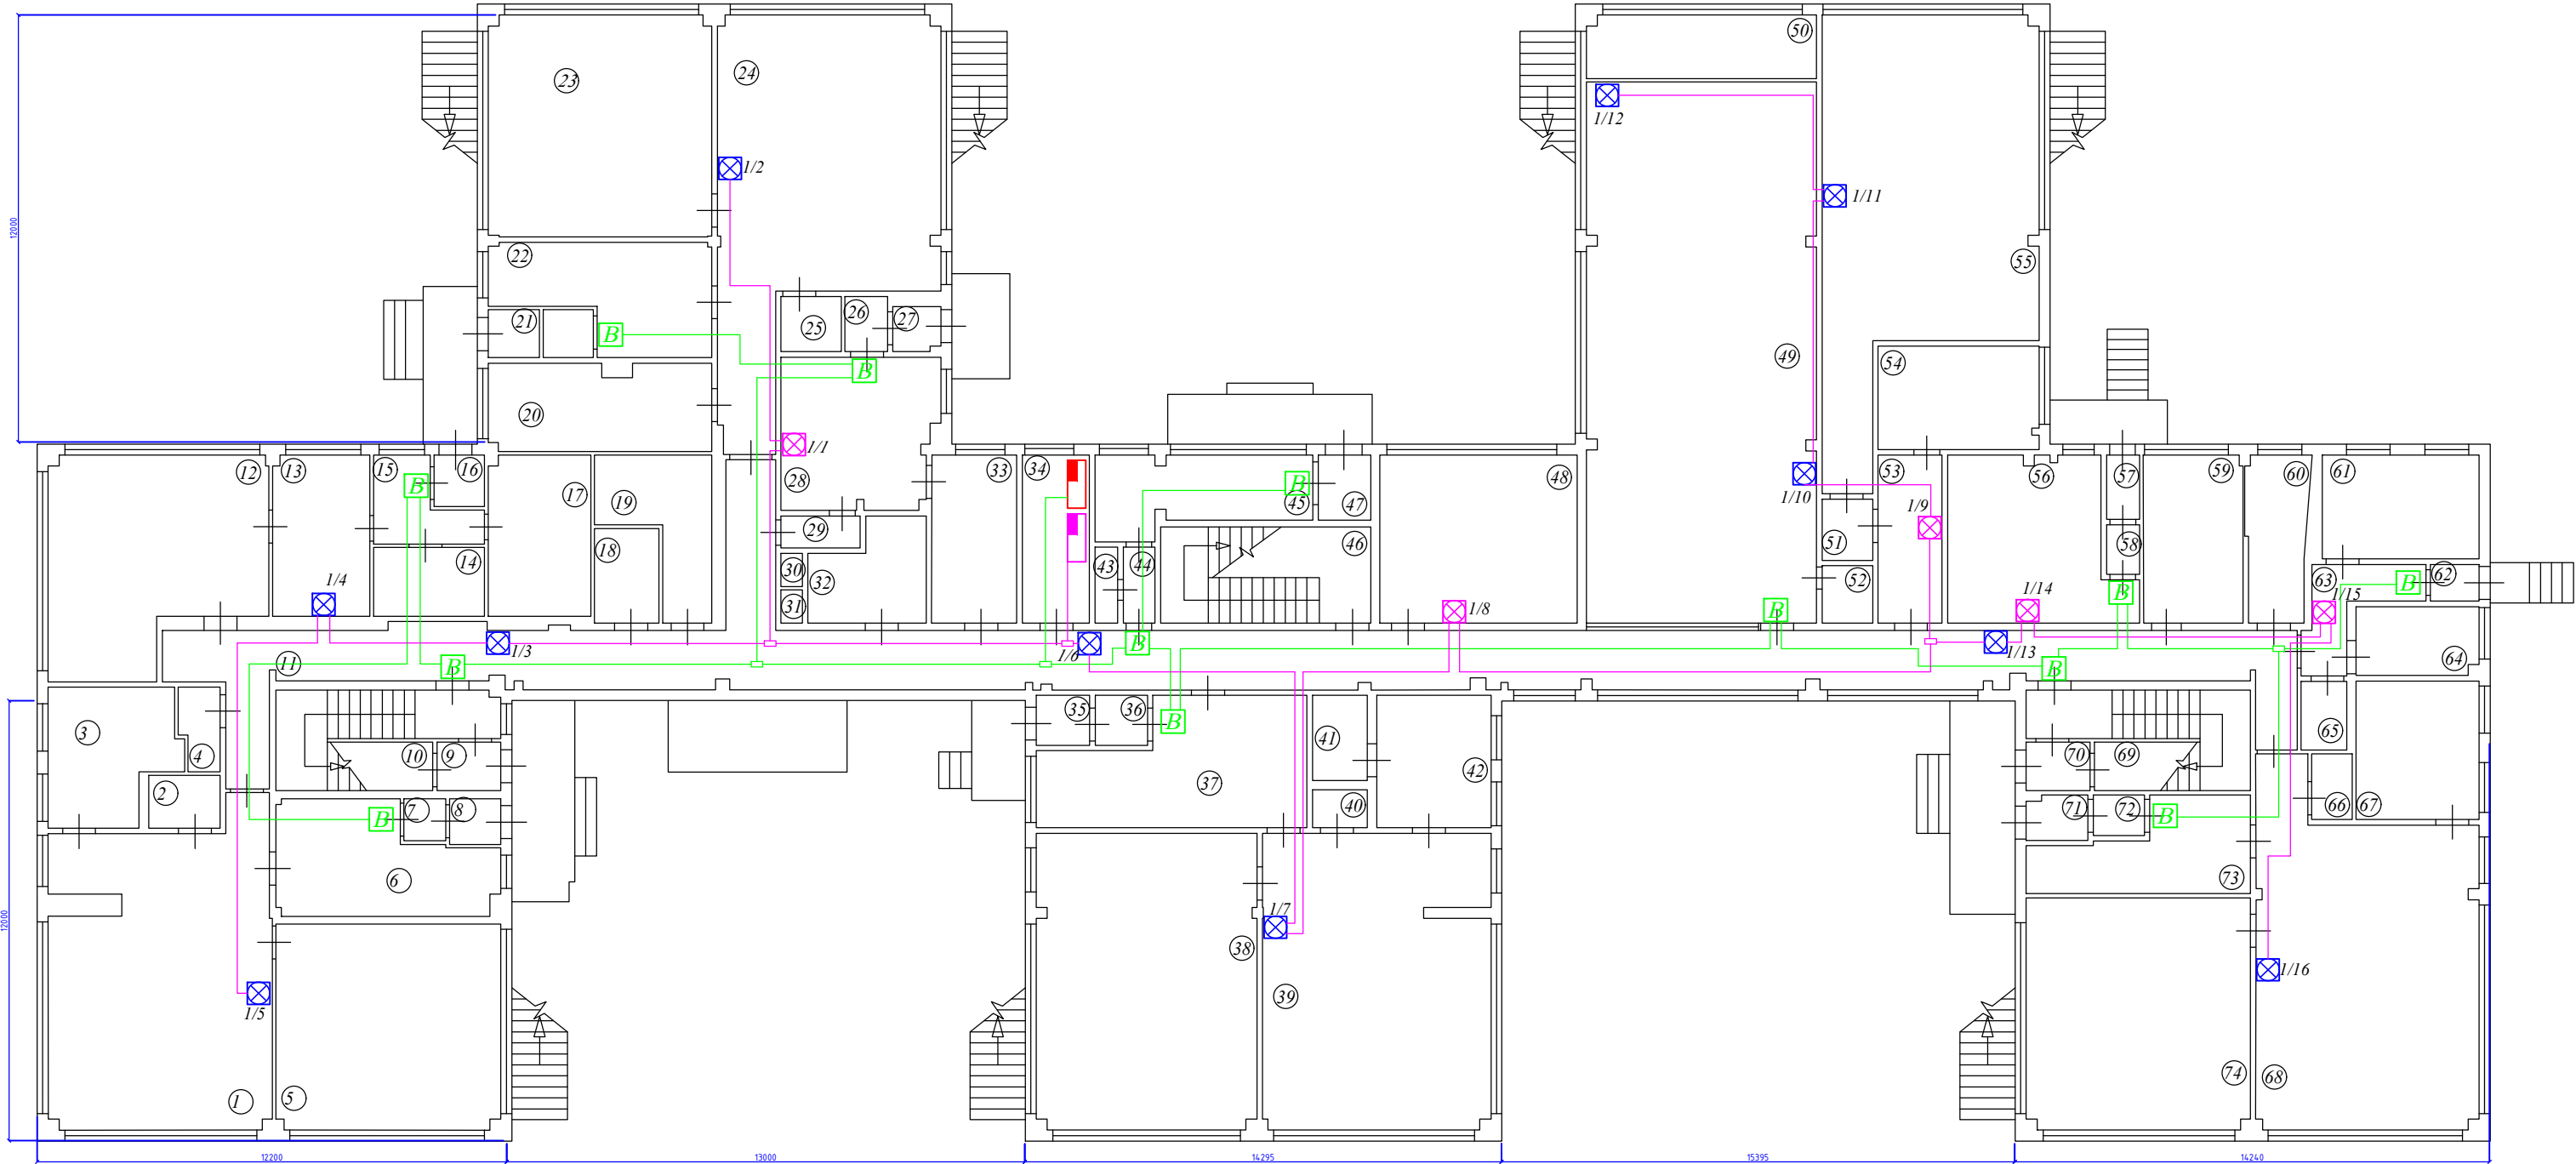

Експлікація приміщень			Експлікація приміщень			Експлікація приміщень		
№	Назва приміщення	Площа, кв. м	№	Назва приміщення	Площа, кв. м	№	Назва приміщення	Площа, кв. м
1	Ігрова кімната	48,6	26	Тамбур	1,7	53	Коридор	7,8
2	Мийка	2,3	27	Тамбур	1,6	54	Кабінет	12
3	Санвузол	11,7	28	Пральня	17,2	55	Спортивний зал	58,5
4	Роздягальня	2,3	29	Коридор	1,9	56	Кабінет	20,1
5	Кімната відпочинку	35,9	30	Електрощитова	0,6	57	Тамбур	1,6
6	Роздягальня	15,2	31	Електрощитова	0,6	58	Тамбур	1,2
7	Тамбур	1,3	32	Кабінет	8	59	Кабінет	12,6
8	Тамбур	1,7	33	Кабінет	10,7	60	Кабінет	7,3
9	Тамбур	2,3	34	Кабінет	8,5	61	Медпункт	17,1
10	Сходи	13,9	35	Тамбур	1,9	62	Тамбур	1,3
11	Коридор	101,9	36	Тамбур	2	63	Коридор	5,1
12	Кухня	32,5	37	Роздягальня	22	64	Кабінет	6,1
13	Обочевий цех	12,2	38	Кімната відпочинку	48,8	65	Санвузол	1,9
14	Підсобне	4,6	39	Ігрова кімната	45,3	66	Мийка	2,4
15	Коридор	5	40	Мийка	1,6	67	Санвузол	12,1
16	Тамбур	1,9	41	Санвузол	3,8	68	Ігрова кімната	52
17	Комора	11,4	42	Умивальник	11,3	69	Сходи	13,9
18	Побутове приміщення	4,2	43	Санвузол	1,3	70	Тамбур	2,3
19	Склад	9,6	44	Коридор	1,8	71	Тамбур	2
20	Санвузол	16	45	Кабінет	11,1	72	Тамбур	1,5
21	Тамбур	1,8	46	Сходи	11,1	73	Роздягальня	11,8
22	Роздягальня	16,7	47	Тамбур	2,5	74	Кімната відпочинку	38,5
23	Кімната відпочинку	37,5	48	Кабінет	25,3			
24	Ігрова кімната	51,8	49	Музичний зал	92,3			
25	Мийка	3,1	50	Побутова кімната	10,7			
			51	Коридор	2,3			
			52	Побутова кімната	2,1			

Умовні позначення	
	Моноблок ВЕ.ЛЕЗн 120-100
	Світловий оповіслювач "Вихід"
	Світлозвуковий оповіслювач "Вихід"
	Гучномовець ЗАС100ПН (1Вт)
	Гучномовець ЗАС100ПН (3Вт)
	Кнопка ручного пуску системи оповіщення
	Коробка розподільча 85х85
	Провід JE-H(Si)H/E 30 1х2х0,8

						03/2026-СПС-СО		
						Монтаж автоматичної пожежної сигналізації в закладі дошкільної освіти №21 "Горобинка", що розташований за адресою: м. Кропивницький, вул. Марії Примаченко, 4. Коригування		
Змін.	Кільк	Арк.	№док	Підпис	Дата			
ГП	Черевань				2026	Система пожежної сигналізації та система керування евакуюванням в частині оповіщення про пожежу	Стадія	Аркуш
Розробив	Патинко				2026		РП	4
Перевірив	Черевань				2026			Аркушів
						Схема СО 1-го поверху	ТОВ "Пожежно-технічний захист"	
Н. Контр.	Черевань				2026			

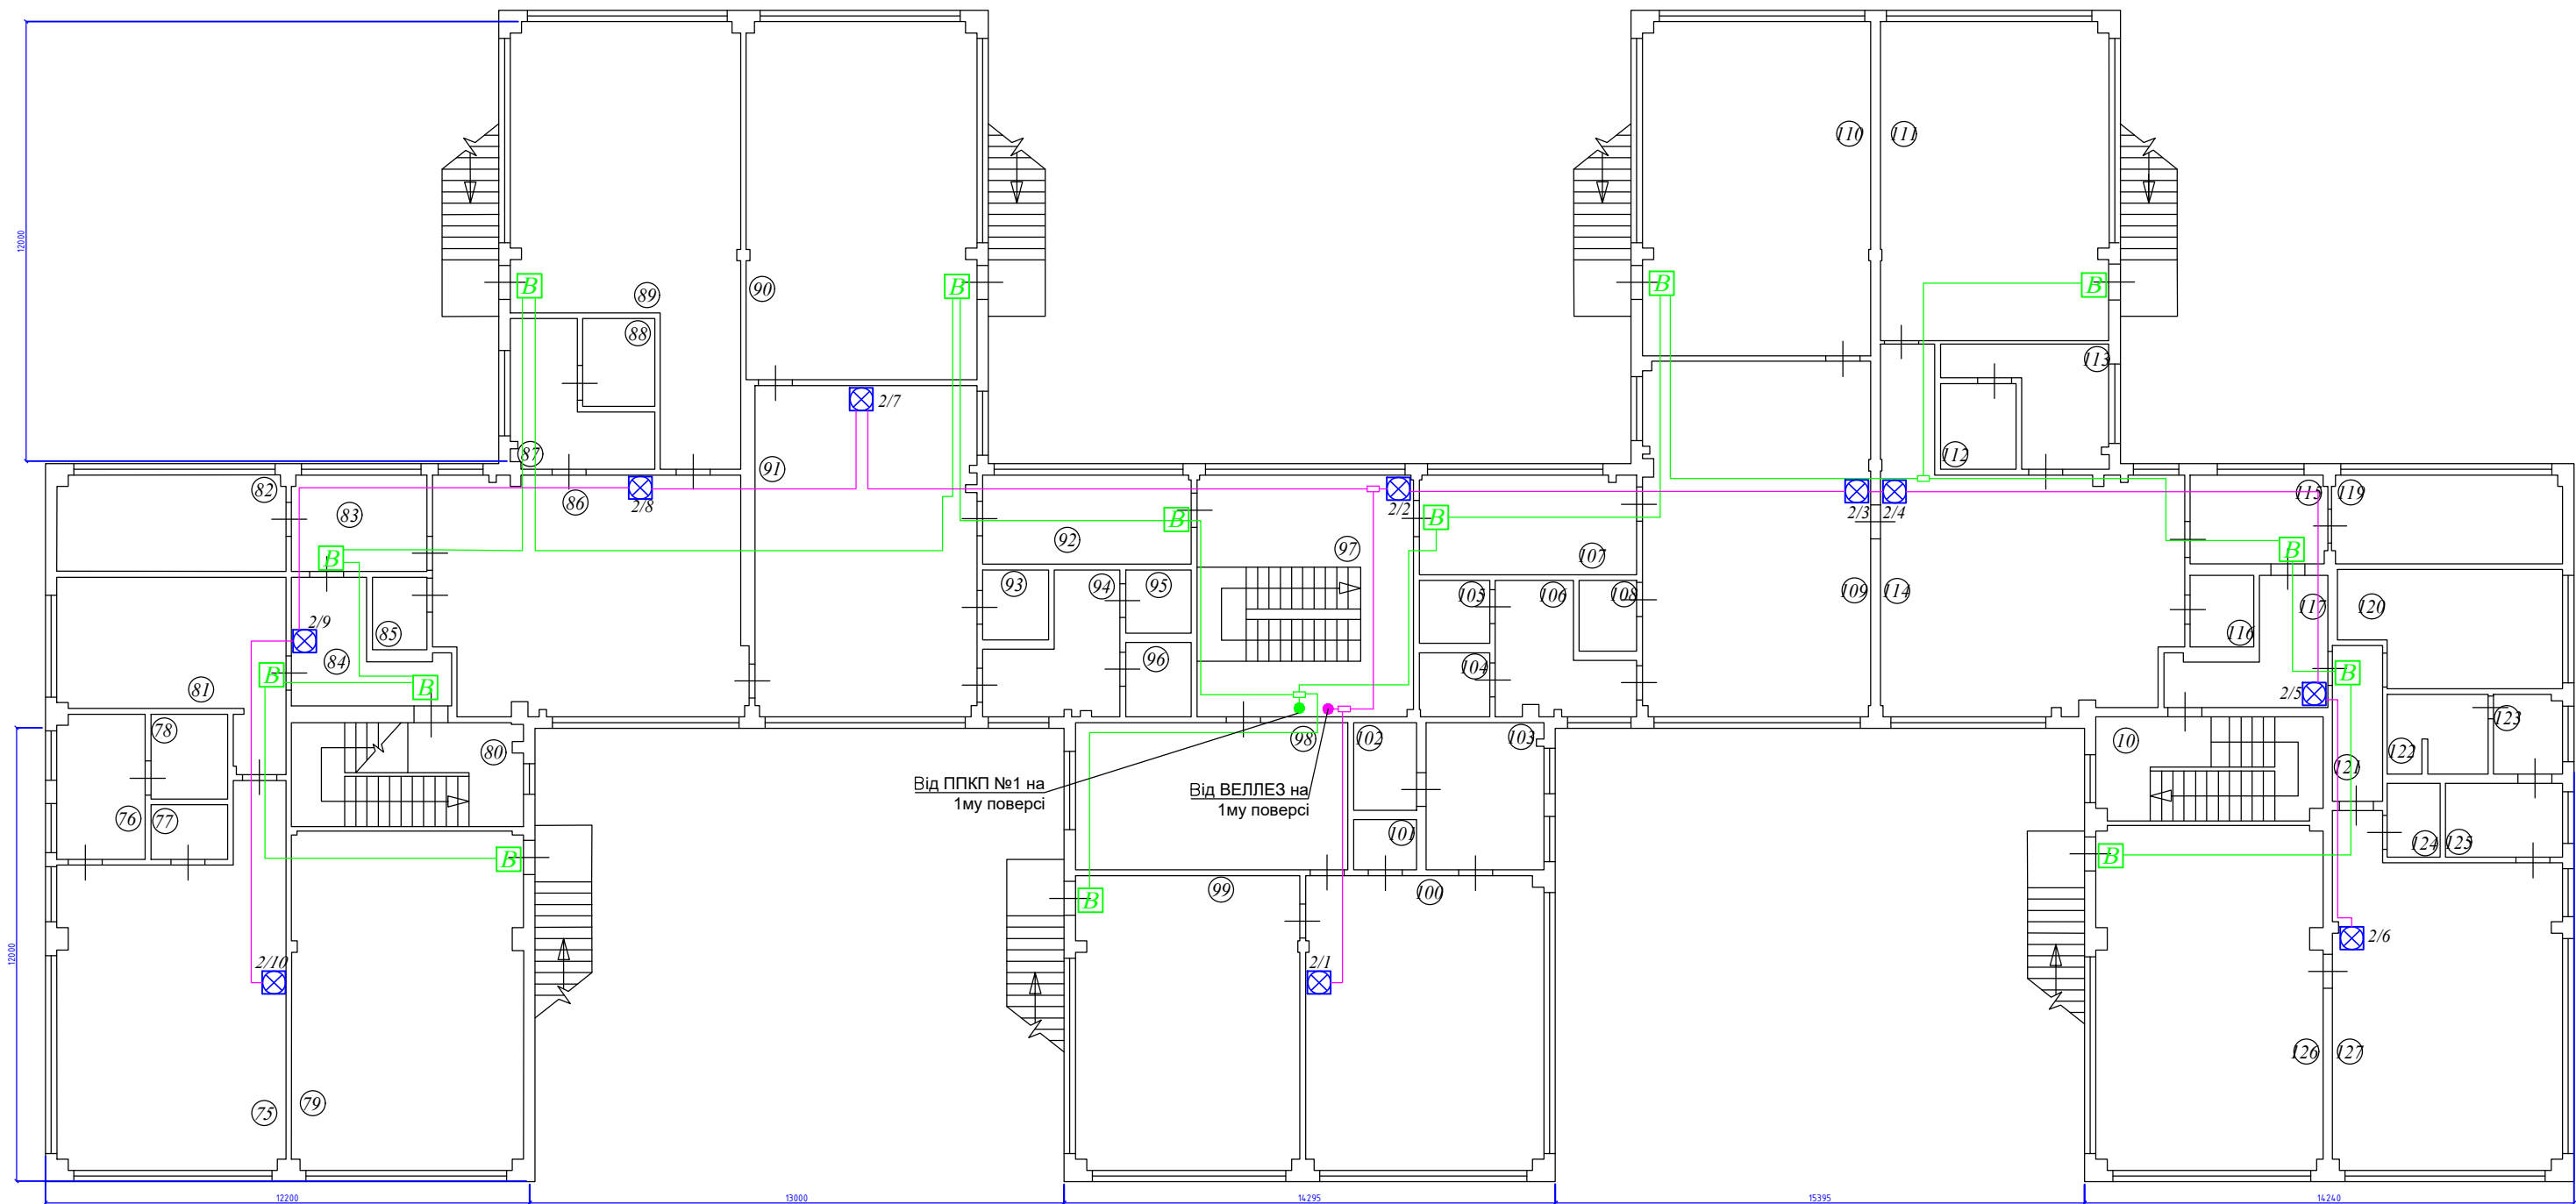


Експлікація приміщень			Експлікація приміщень		
№	Назва приміщення	Площа, кв. м	№	Назва приміщення	Площа, кв. м
75	Ігрова кімната	51,3	100	Ігрова кімната	50,1
76	Умивальник	8,9	101	Мийка	2,2
77	Мийка	2,9	102	Санвузол	3,9
78	Санвузол	4,7	103	Умивальник	11,7
79	Кімната відпочинку	54,8	104	Санвузол	2,9
80	Сходи	17,2	105	Санвузол	3,1
81	Роздягальня	23,4	106	Умивальник	9,8
82	Побутове приміщення	14,9	107	Роздягальня	15,1
83	Коридор	9,1	108	Мийка	2,8
84	Коридор	9,5	109	Ігрова кімната	56,2
85	Побутове приміщення	2,7	110	Кімната відпочинку	53,2
86	Ігрова кімната	51,2	111	Кімната відпочинку	50,7
87	Умивальник	10,1	112	Санвузол	4,5
88	Санвузол	4,4	113	Умивальник	9,5
89	Кімната відпочинку	55,4	114	Ігрова кімната	54,4
90	Кімната відпочинку	57,6	115	Коридор	8,5
91	Ігрова кімната	51,4	116	Побутове приміщення	3,2
92	Роздягальня	13	117	Коридор	9,5
93	Мийка	3,2	118	Сходи	16,1
94	Умивальник	8,7	119	Побутове приміщення	14,2
95	Санвузол	2,8	120	Роздягальня	17,1
96	Санвузол	3	121	Коридор	9,5
97	Сходи	25,8	122	Санвузол	5,1
98	Роздягальня	28,1	123	Умивальник	3,7
99	Кімната відпочинку	47,3	124	Мийка	2,7
			125	Умивальник	5,8
			126	Кімната відпочинку	54,2
			127	Ігрова кімната	51,1

Умовні позначення

	Моноблок ВЕЛЛЕЗ 120-100
	Світловий оповіщувач "Вихід"
	Світлозвуковий оповіщувач "Вихід"
	Гучномовець ЗАС100ПН (1Вт)
	Гучномовець ЗАС100ПН (3Вт)
	Кнопка ручного пуску системи оповіщення
	Коробка розподільча 85x85
	Провід JE-H(St)H/E 30 1x2x0,8

						03/2026-СПС-СО				
						Монтаж автоматичної пожежної сигналізації в закладі дошкільної освіти №21 "Горобинка", що розташований за адресою: м. Кропивницький, вул. Марії Примаченко, 4. Коригування				
Змін.	Кільк.	Арк.	№док	Підпис	Дата	Система пожежної сигналізації та система керування евакуюванням в частині оповіщення про пожежу		Стадія	Аркуш	Аркушів
ГП		Черевань			2026			РП	5	6
Розробив		Патинко			2026					
Перевірив		Черевань			2026	Схема СО 2-го поверху		ТОВ "Пожежно-технічний захист"		
Н. Контр.		Черевань			2026					

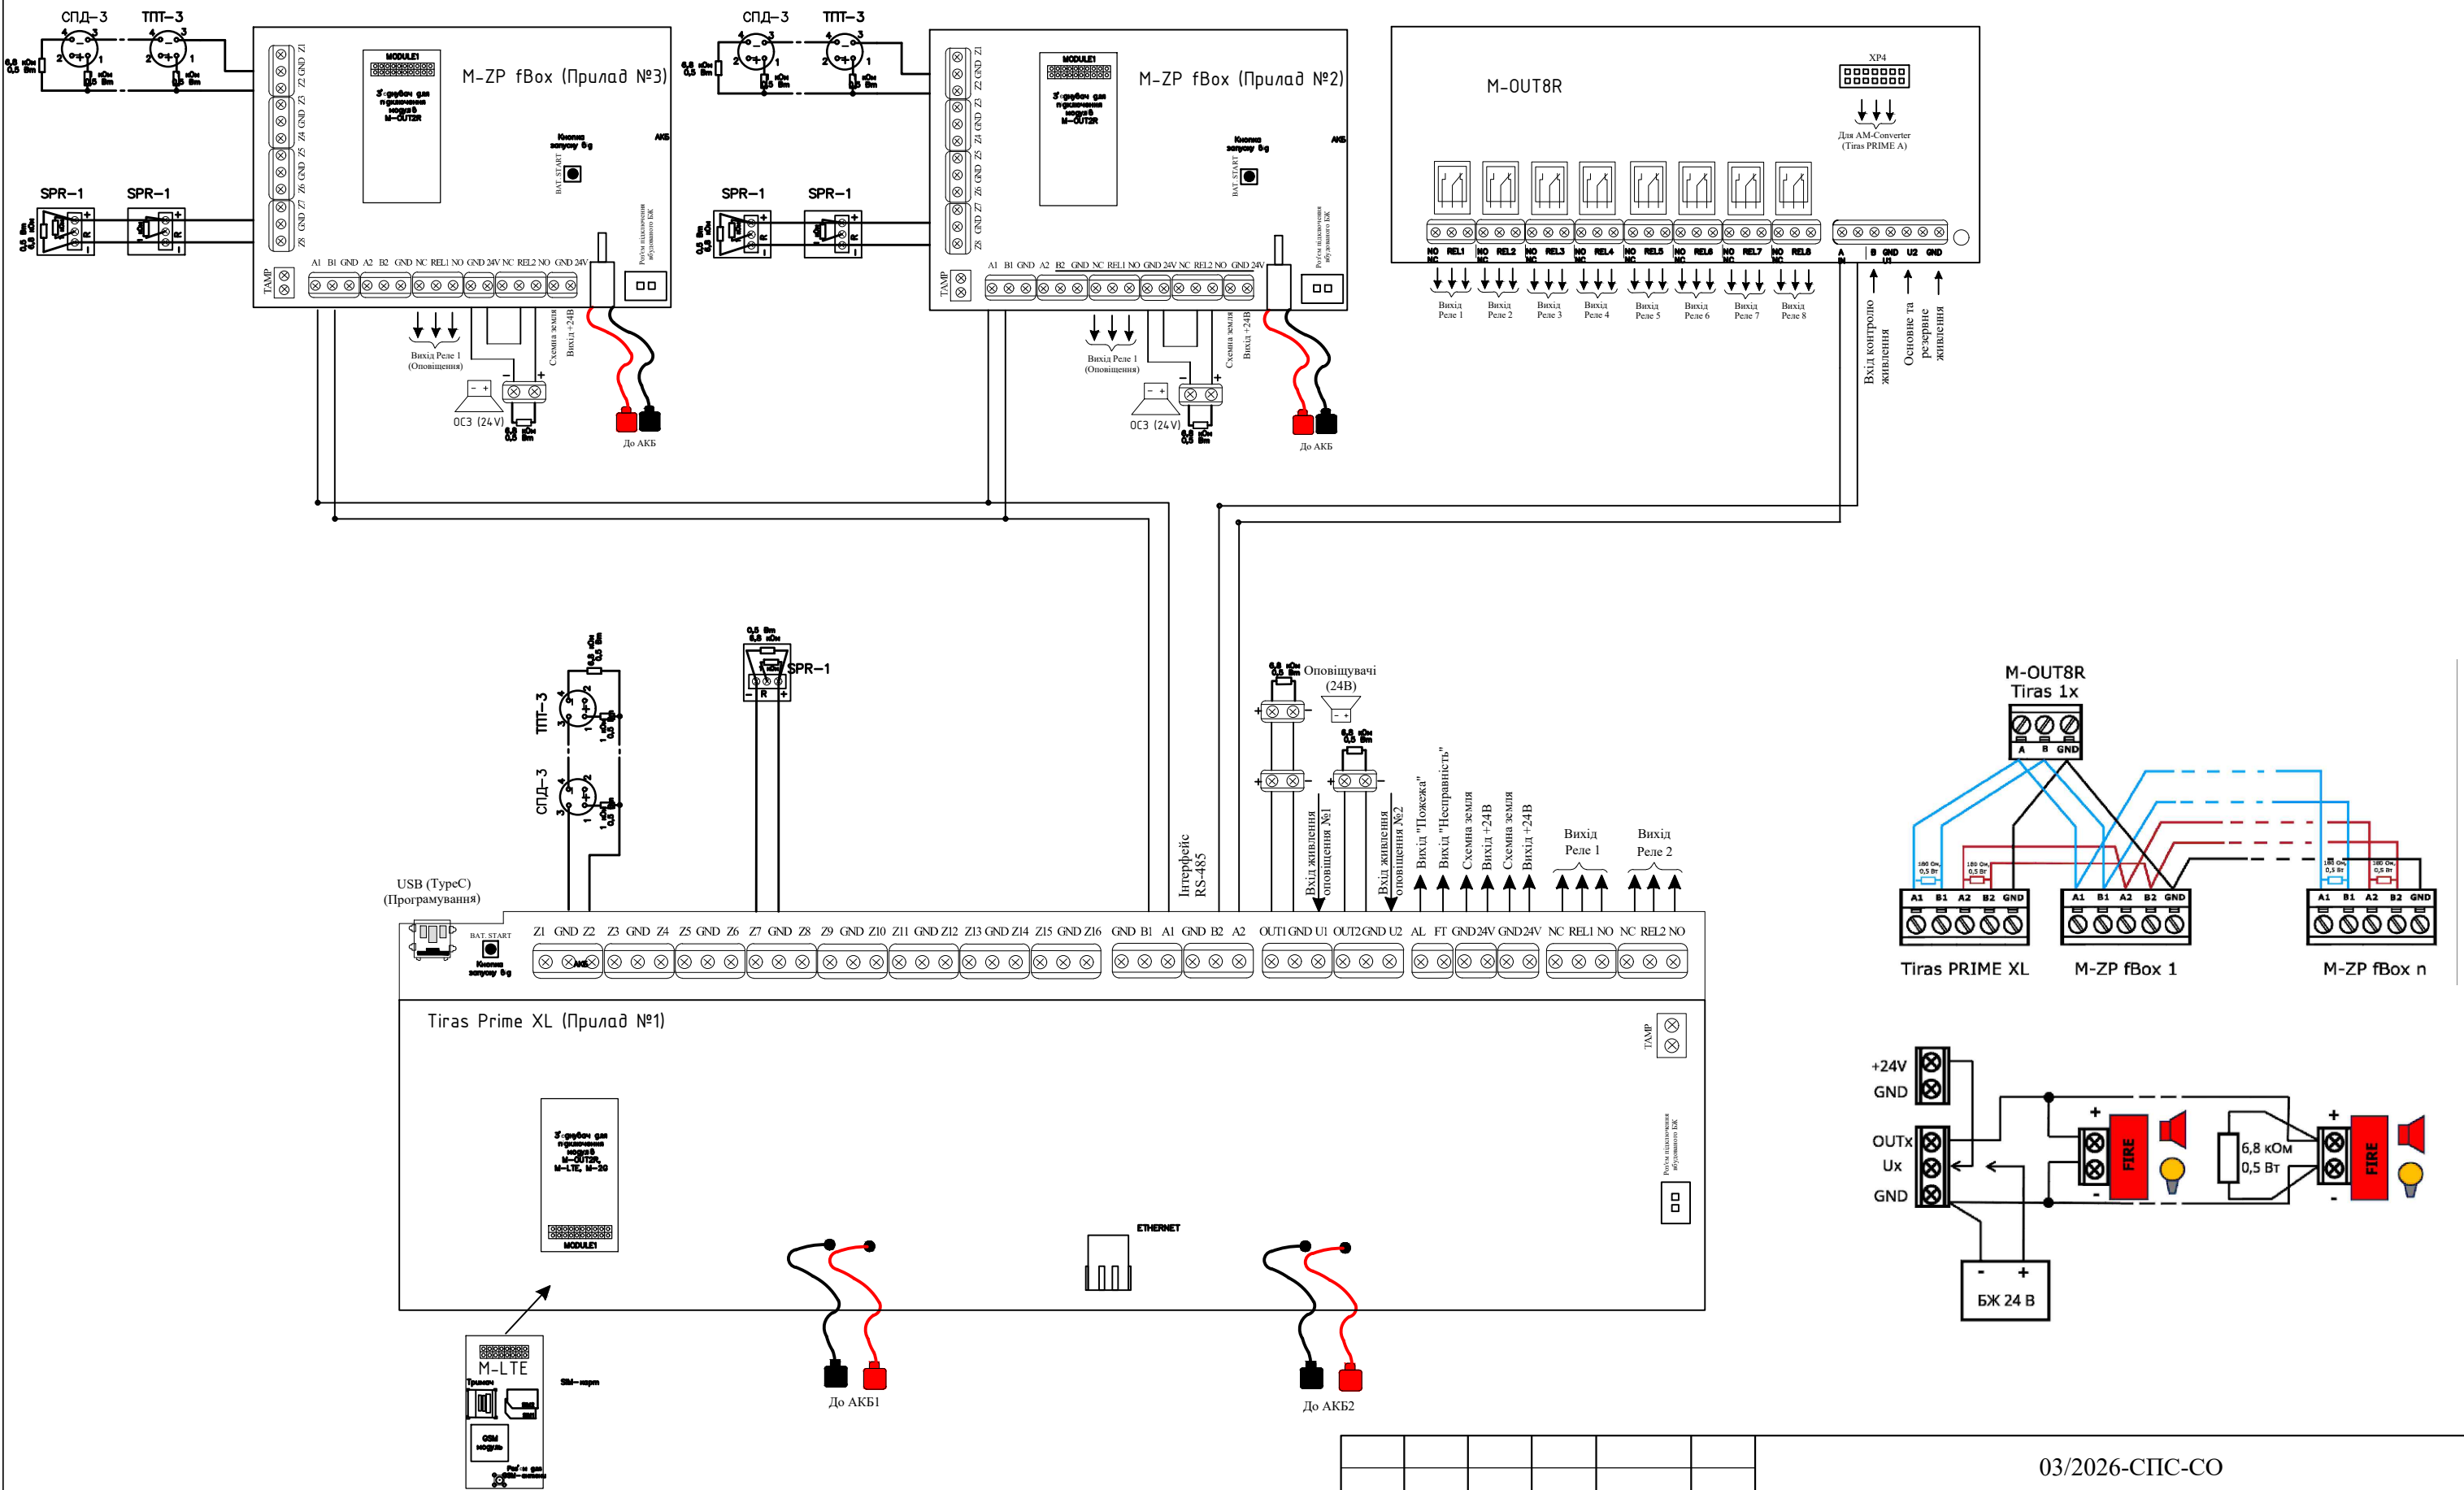

						03/2026-СПС-СО				
						Монтаж автоматичної пожежної сигналізації в закладі дошкільної освіти №21 "Горобинка", що розташований за адресою: м. Кропивницький, вул. Марії Примаченко, 4. Коригування				
Змін.	Кільк	Арк.	№док	Підпис	Дата					
ГП		Черевань			2026	Система пожежної сигналізації та		Стадія	Аркуш	Аркушів
Розробив		Патинко			2026	система керування евакууванням в частині оповіщення про пожежу		РП	6	6
Перевірив		Черевань			2026					
Н. Контр.		Черевань			2026	Схема електричних з'єднань		ТОВ "Пожежно-технічний захист"		